Перв. примен.

Справ. №

Подп. и дата

Инв. № дубл.

Взам. инв. №

Подп. и дата

Инв. № подл.

Фрагмент плана 1-го этажа отм. 0.000
Масштаб 1:100

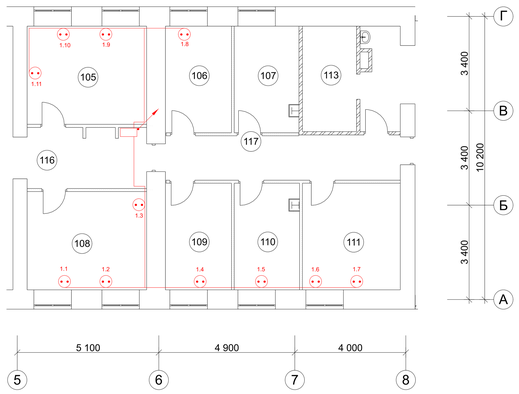

ЭКСПЛИКАЦИЯ ПОМЕЩЕНИЙ

№ п/пл.	Наименование	Площадь М2	№ п/пл.	Наименование	Площадь М2
101	Тамбур	4,7	111	Офисное помещение	13,1
102	Вестибюль	13,8	112	Комната приема пищи	16,8
103	Помещение охраны	13,4	113	Насосная	6,9
104	Выставочный зал	111,1	114	Электрощитовая	8,2
105	Офисное помещение	15,2	115	Санитарный узел	8,3
106	Офисное помещение	9,1	116	Коридор	9,2
107	Тепловой пункт	9,1	117	Коридор	14,1
108	Офисное помещение	15,2	118	Лестничная клетка №1	11,8
109	Офисное помещение	9,1	119	Лестничная клетка №2	15,7
110	Офисное помещение	9,1			

Условные обозначения:

- Розетка RJ45
- Шкаф коммуникационный №1
- Кабельный лоток 100х100.

Примечания:
Прокладку металических, кабельных лотков осуществлять за подшивным потолком, крепить к перекрытиям.
Опуски к розеткам осуществлять в гофрированной трубе диаметром 16 мм. скрыто в стене.

Изм	Лист	№ докум.	Подпись	Дата				
					3/20.03.05-ЛВС			
					г. Симферополь, пр. Мира д.10			
ГИП		Смирнов			Реконструкция здания с надстройкой двумя этажами и мансардой	Стадия	Лист	Листов
Инженер		Иванов				РД	12	
					Размещение оборудования локальной вычислительной сети на 1 этаже	ООО "Авангард"		

Формат А3

Фрагмент плана 2-го этажа отм. 3.600
Масштаб 1:100

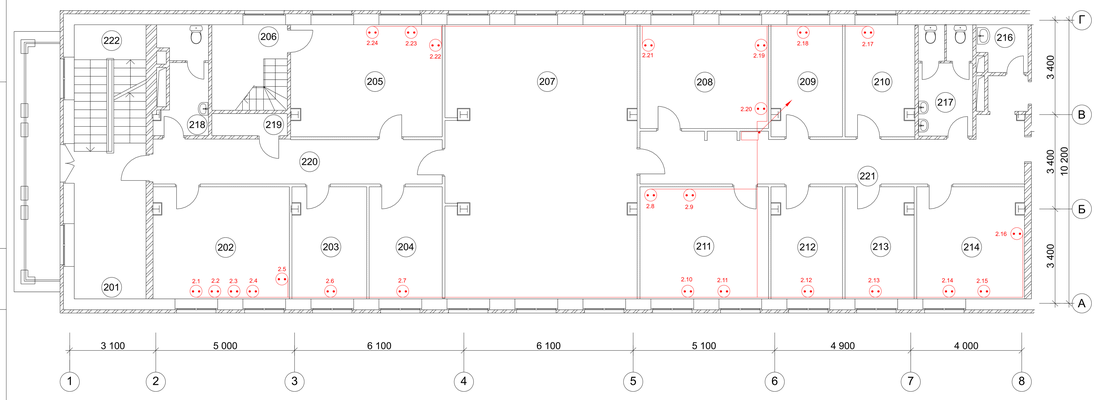

ЭКСПЛИКАЦИЯ ПОМЕЩЕНИЙ

№ п/пл.	Наименование	Площадь М2	№ п/пл.	Наименование	Площадь М2
201	Холл	10,4	213	Офисное помещение	10,0
202	Офисное помещение	19,8	214	Офисное помещение	15,7
203	Офисное помещение	10,7	215	Офисное помещение	9,4
204	Офисное помещение	10,5	216	Кладовая уборочного инвентаря	2,8
205	Кабинет директора	21,8	217	Санитарный узел	7,7
206	Лестница	8,3	218	Санитарный узел	8,0
207	Выставочный зал	68,2	219	Подсобное помещение	1,7
208	Офисное помещение	18,2	220	Коридор	16,6
209	Офисное помещение	10,0	221	Коридор	26,3
210	Офисное помещение	10,0	222	Лестница №1	16,6
211	Офисное помещение	19,4	223	Лестница №2	26,3
212	Офисное помещение	10,0			

Условные обозначения:

- Розетка RJ45
- Шкаф коммуникационный №2
- Кабельный лоток 100х100.

Примечания:
Прокладку металических, кабельных лотков осуществлять за подшивным потолком, крепить к перекрытиям.
Опуски к розеткам осуществлять в гофрированной трубе диаметром 16 мм. скрыто в стене.

Изм	Лист	№ докум.	Подпись	Дата				
					3/20.03.05-ЛВС			
					г.Симферополь, пр. Мира д.10			
ГИП		Смирнов			Реконструкция здания с надстройкой двумя этажами и мансардой	Стадия	Лист	Листов
Инженер		Иванов				РД	13	
					Размещение оборудования локальной вычислительной сети на 2 этаже	ООО "Авангард"		

Формат А3